
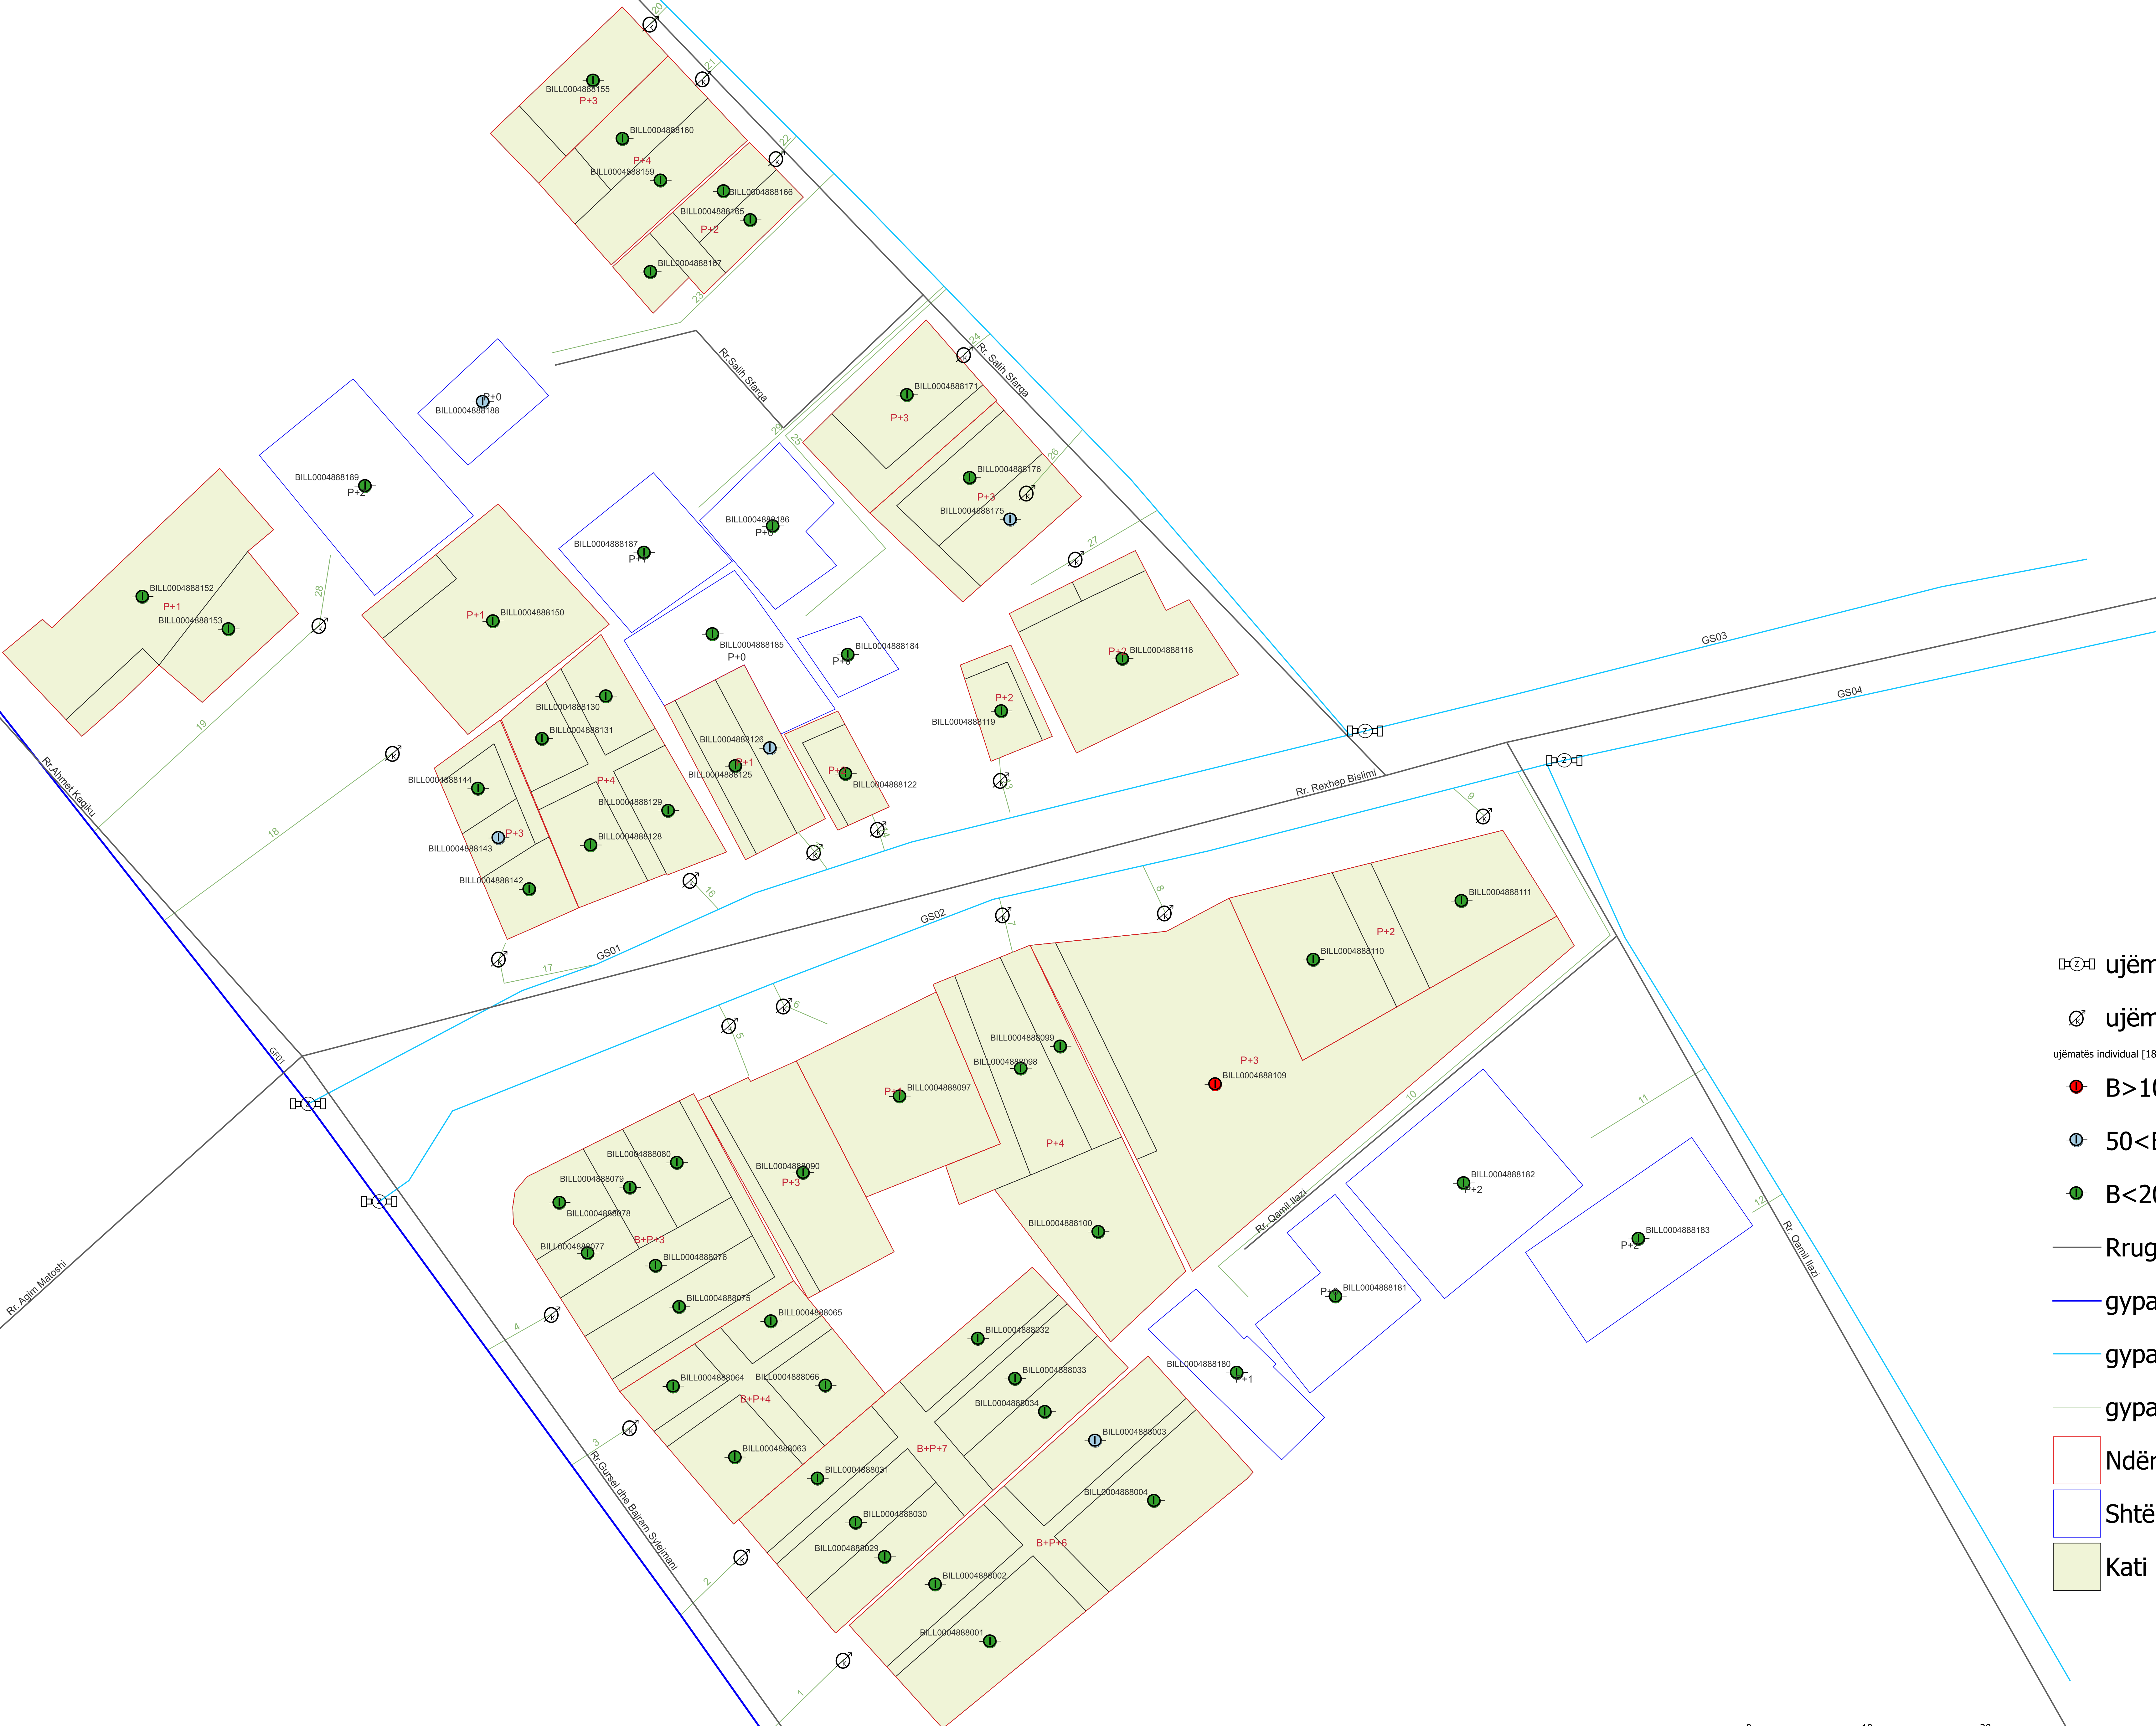


Rrjeti i ujësjellësit Ferizaj / Harta e borgjeve / Përdhesa

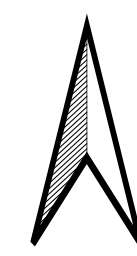

- ujëmatës zonal [4]
- ujëmatës kolektiv [22]
- ujëmatës individual [189]
- B>100 [1]
- 50<B>20 [5]
- B<20 [56]
- Rrugët [8]
- gypat furnizues [1]
- gypat shpërndarës [4]
- gypat lidhës
- Ndërtesat [22]
- Shtëpitë [10]
- Kati përdhese [74]

0 10 20 m